
G1-01 / MARKING APPLICATION

標線條文運用解說

G1-01 / 市區・正交

01 / 09　標線

G1-01 / 路面邊線

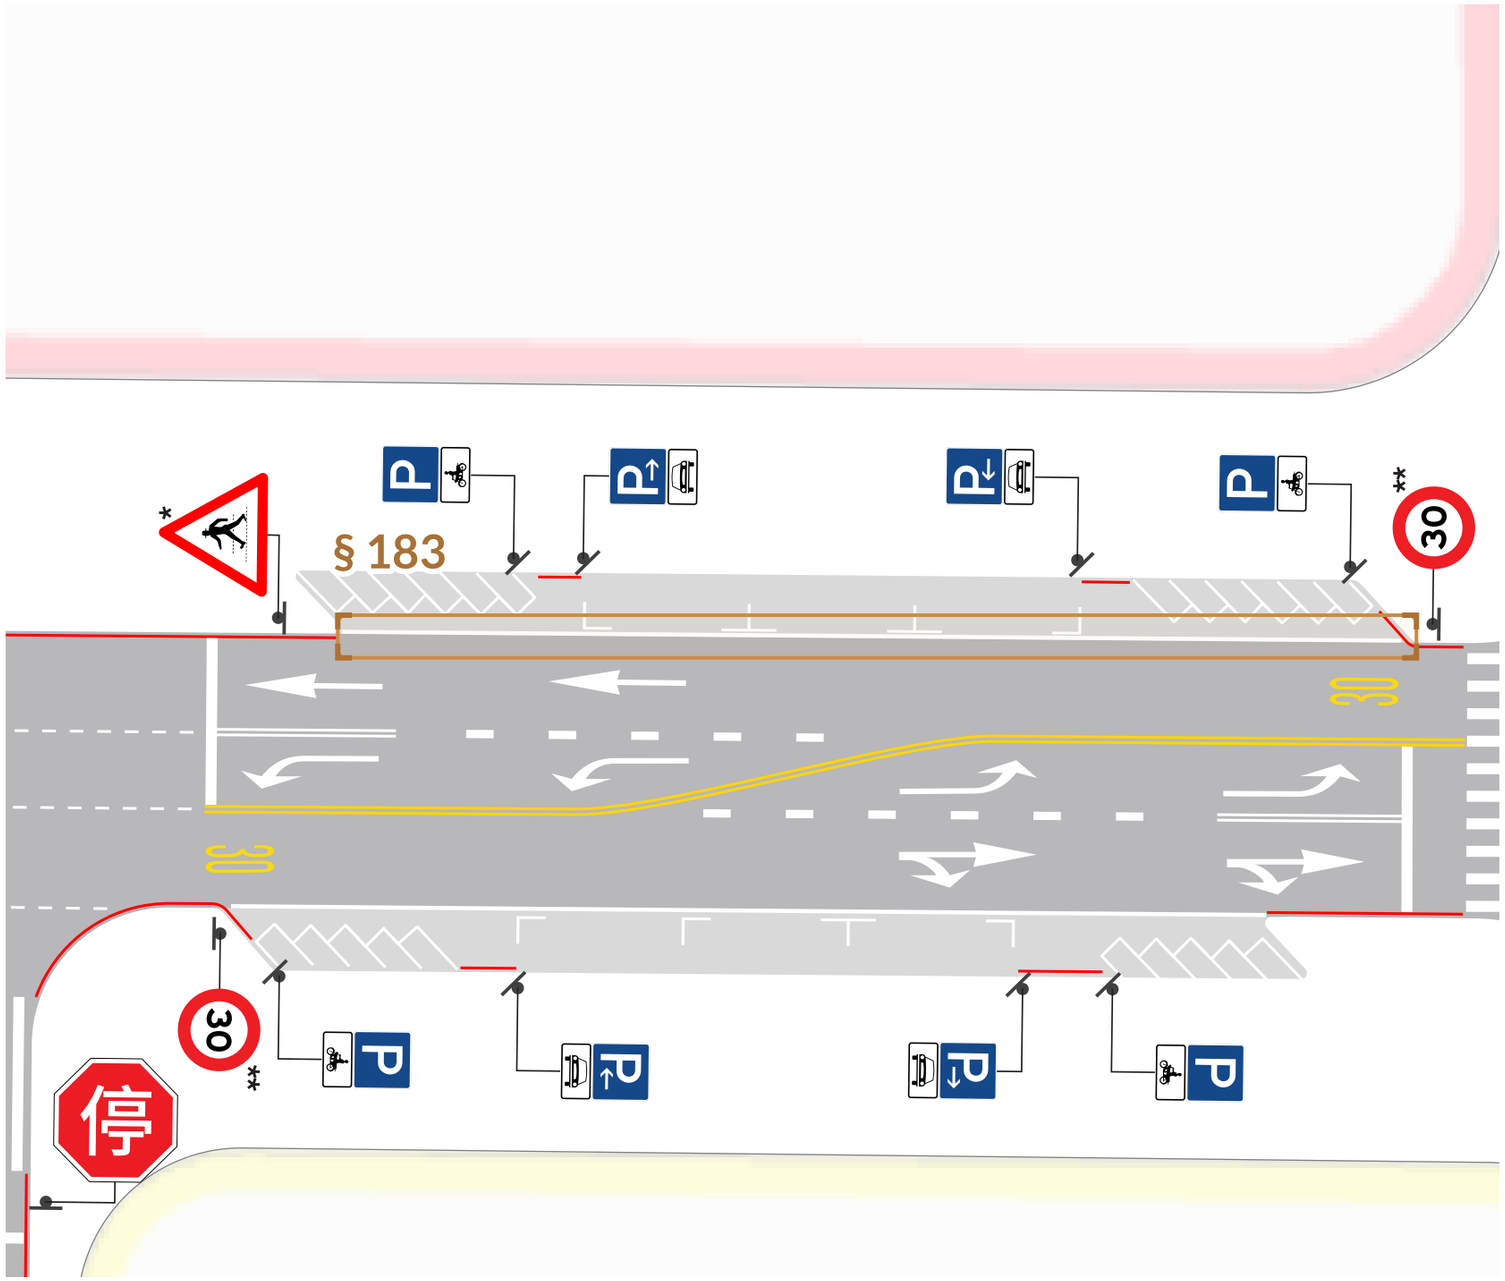

《設置規則》§ 183

路面邊線

01 作為最右側車道的行車導引，界定行車道與路側服務空間。

02 本指引建議停放線與路面邊線保留約 30 cm 緩衝，並讓路段邊線接續路口轉角的邊線。

03 路面邊線為 15 cm；應與 10 cm 的快慢車道分隔線區分。

辨識線寬，也要辨識它界定的是車道還是路肩。