
G1-01 / MARKING APPLICATION

標線條文運用解說

G1-01 / 市區・正交

02 / 09　標線

G1-01 / 枕木紋行人穿越道線

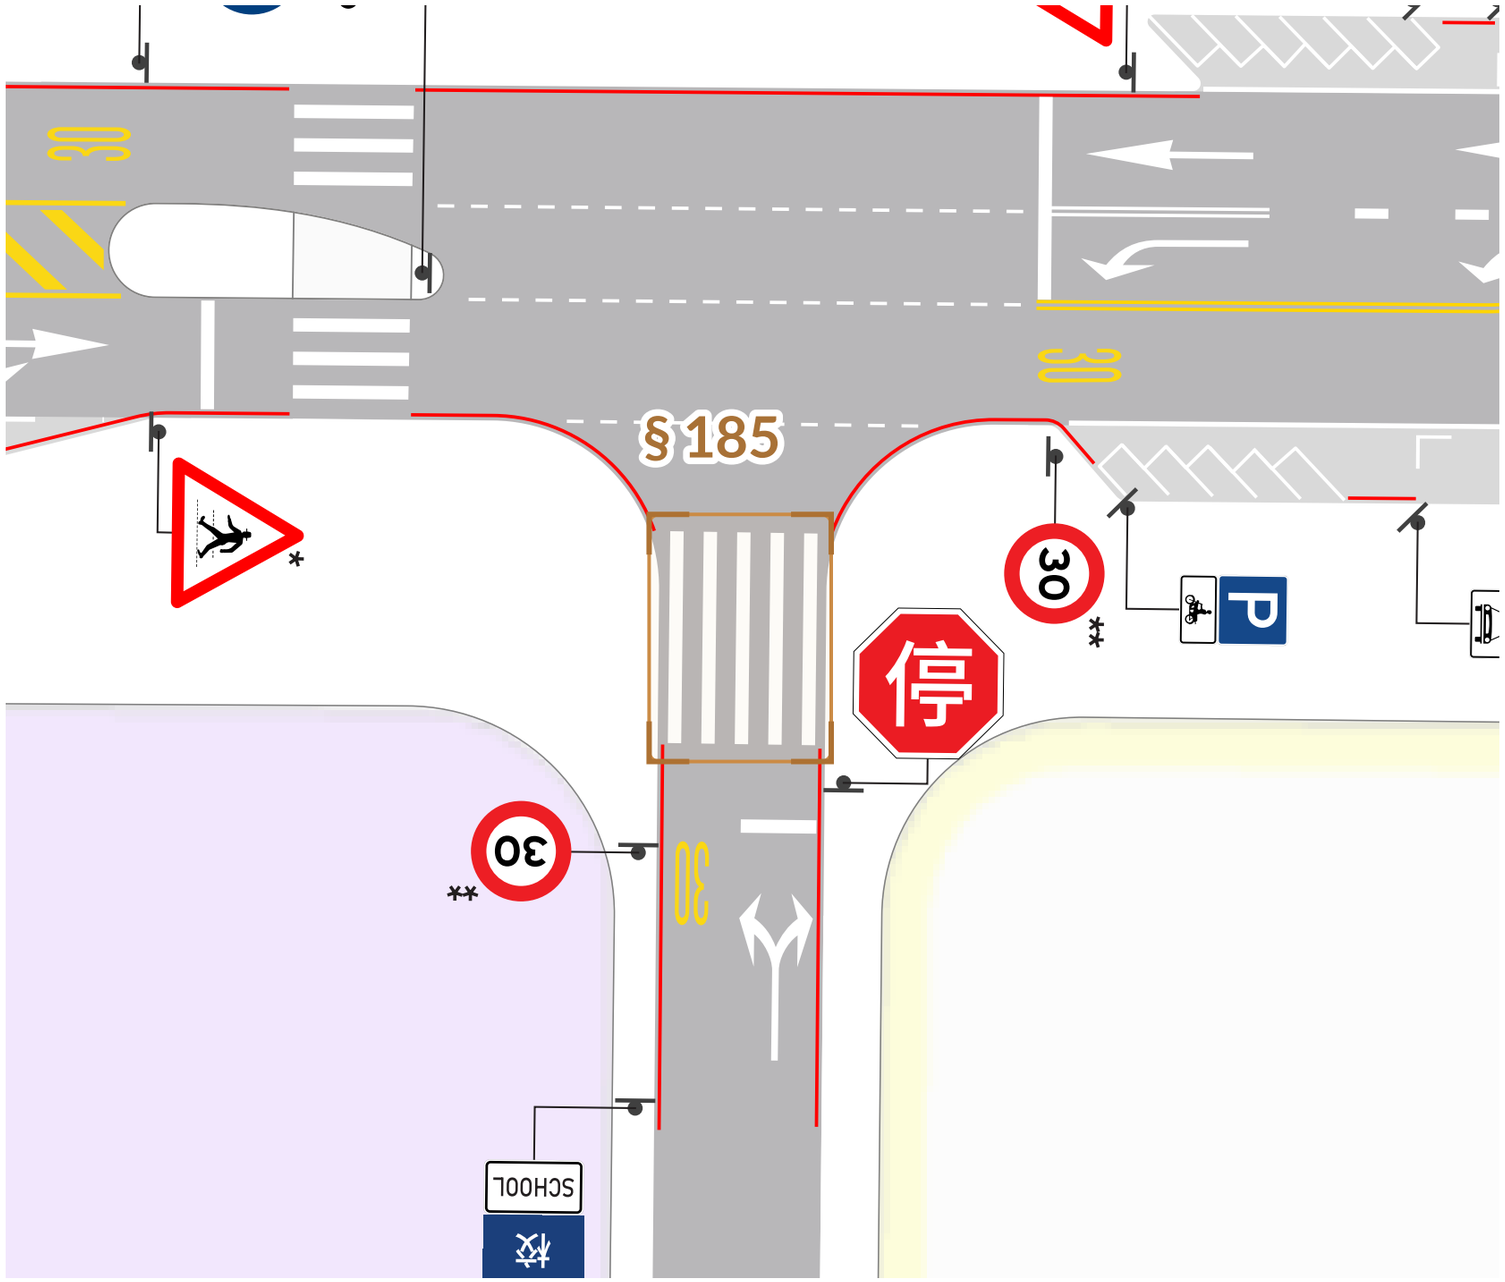

《設置規則》§ 185

枕木紋行人穿越道線

01 本示例配合當心行人標誌「警34」，提高無號誌行穿線的明視度。

02 指引建議枕木紋平行車流方向劃設，並從人行道或路側邊緣開始繪設。

03 較大主次道路交叉口可退縮 3 至 5 m，由路緣量至行穿線上緣，供右轉車停讓。

位置的判斷重點：轉彎車能看見行穿線及正要穿越的行人。