G1-01 / MARKING APPLICATION

標線條文運用解說

G1-01 / 市區・正交

02 / 09　標線

G1-01 / 枕木紋行人穿越道線

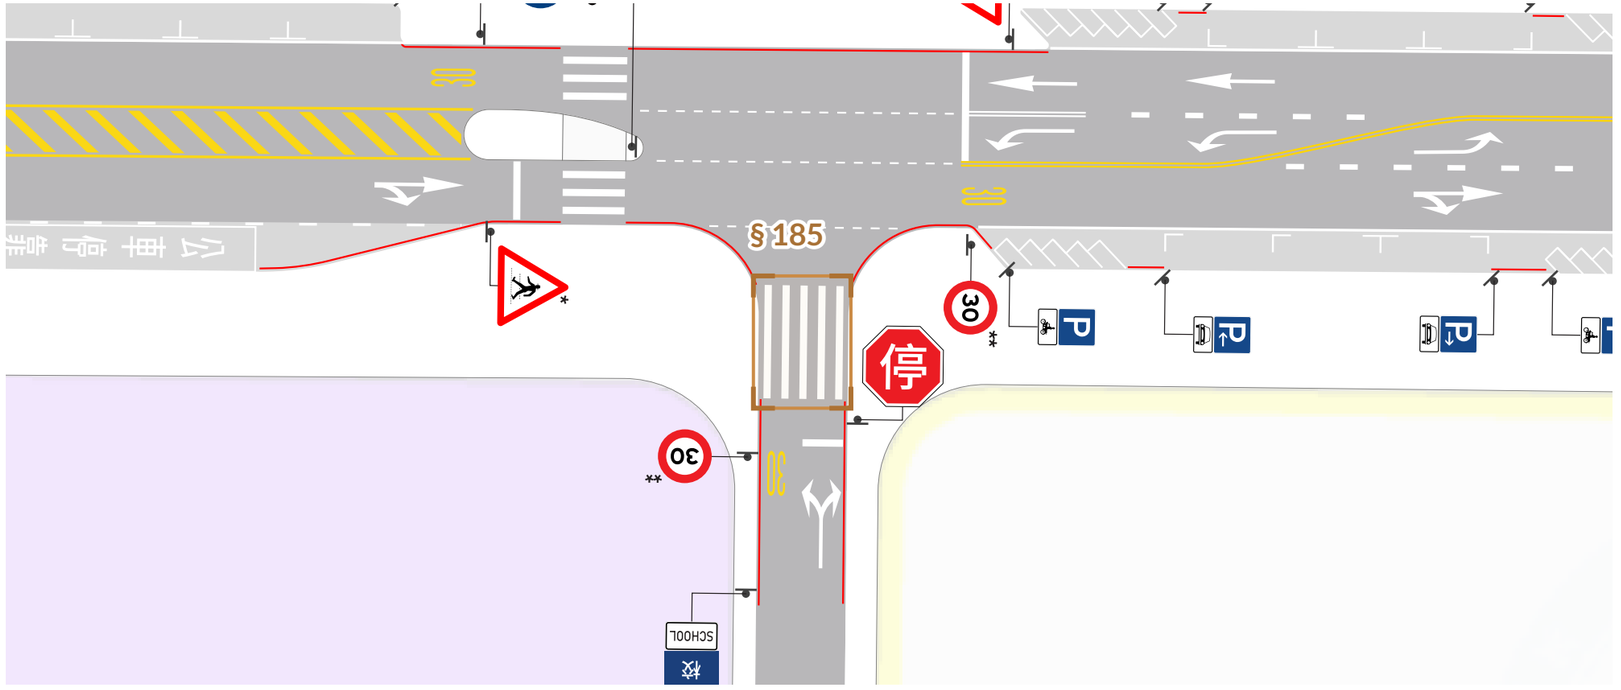


圖 4.1 / 原始 SVG 圖面

《設置規則》§ 185

枕木紋行人穿越道線

01　可配合設置當心行人標誌「警34」警告車輛注意行人通過。

02　枕木紋平行車流方向劃設。

03　枕木紋行人穿越道線與停止線建議 2 至 3 m。

位置的判斷重點：轉彎車能看見行穿線及正要穿越的行人。