G1-01 / MARKING APPLICATION

標線條文運用解說

G1-01 / 市區・正交

03 / 09　標線

G1-01 / 指向線

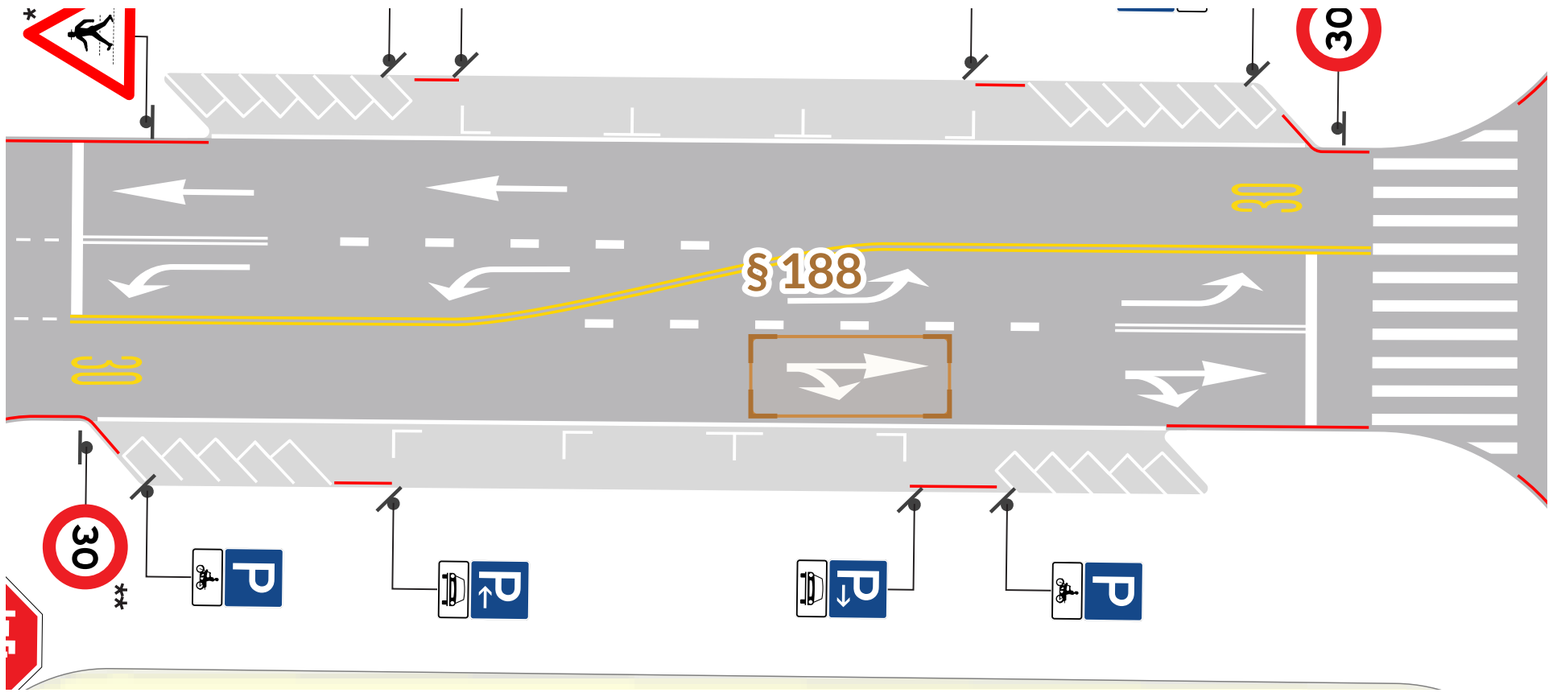


圖 4.1 / 原始 SVG 圖面

《設置規則》§ 188

指向線

01　本示例直右共用混合車道寬度為 3.5 m 以下，使用直線與弧形合併的分岔箭頭。

02　車道寬度為 3.5 m 以上時，使用直線與弧形分離、並列的分流式指向線。

先確認車道寬度，再選擇對應的箭頭配置。