G1-01 / MARKING APPLICATION

標線條文運用解說

G1-01 / 穿越虛線

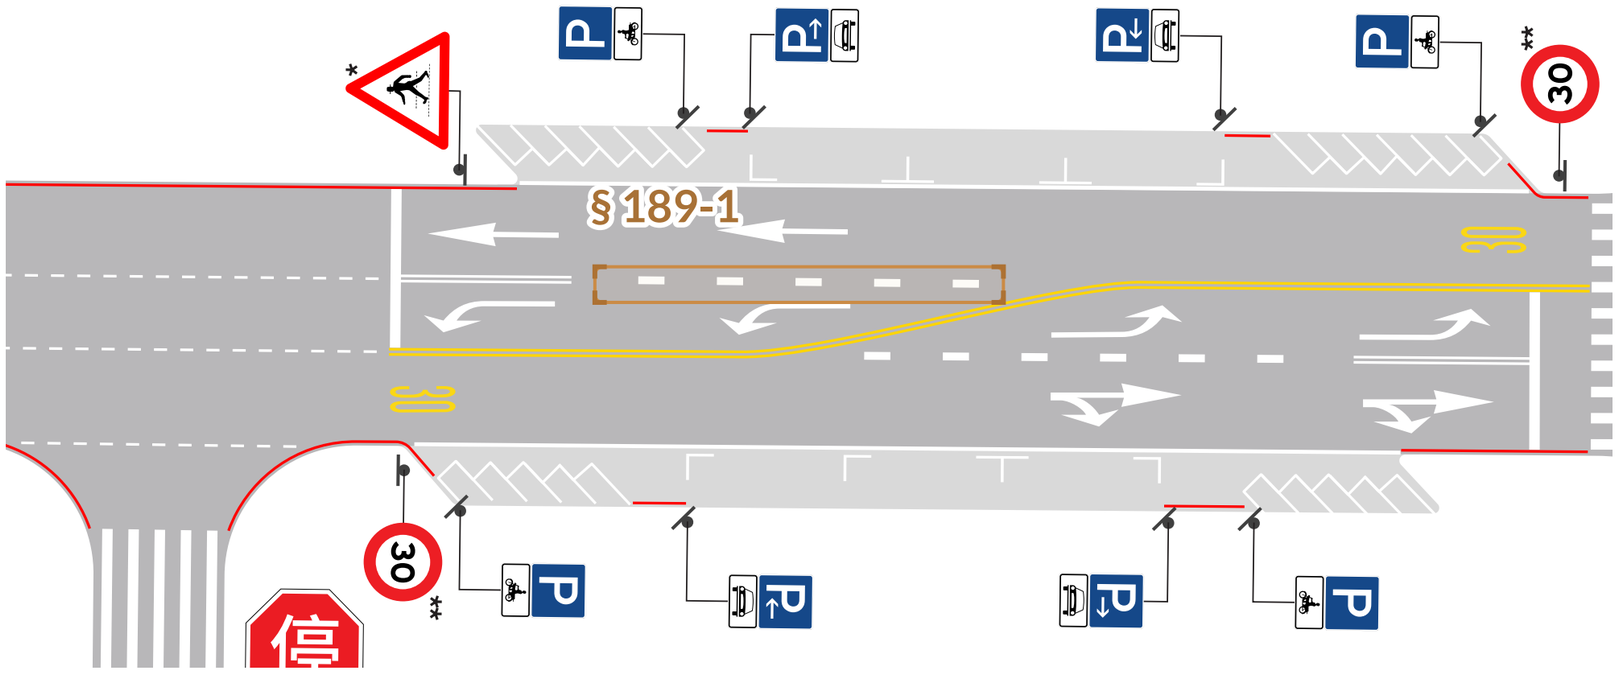


圖 4.1 / 原始 SVG 圖面

《設置規則》§ 189-1

穿越虛線

01 由 1直行車道轉換為直行、左轉 2 車道時，提示左轉車可匯出至專用道。

02 原則上由漸變區起點劃至專用車道起點，提示左轉車打方向燈並分流。

03 本例屬市區道路，漸變長度依《市區道路及附屬工程設計規範》第 4.2.6 節；省道公路另依《公路路線設計規範》第 4.2.10 節。

透過左彎附加車道，提供左轉停等空間並維持直行續進。