
G1 / G1-01 / URBAN T-INTERSECTION

無號誌市區正交三岔路口

市區住宅與商業集結區域。從現況路型出發，檢視路權、行人穿越與行車空間的配置。

現況圖

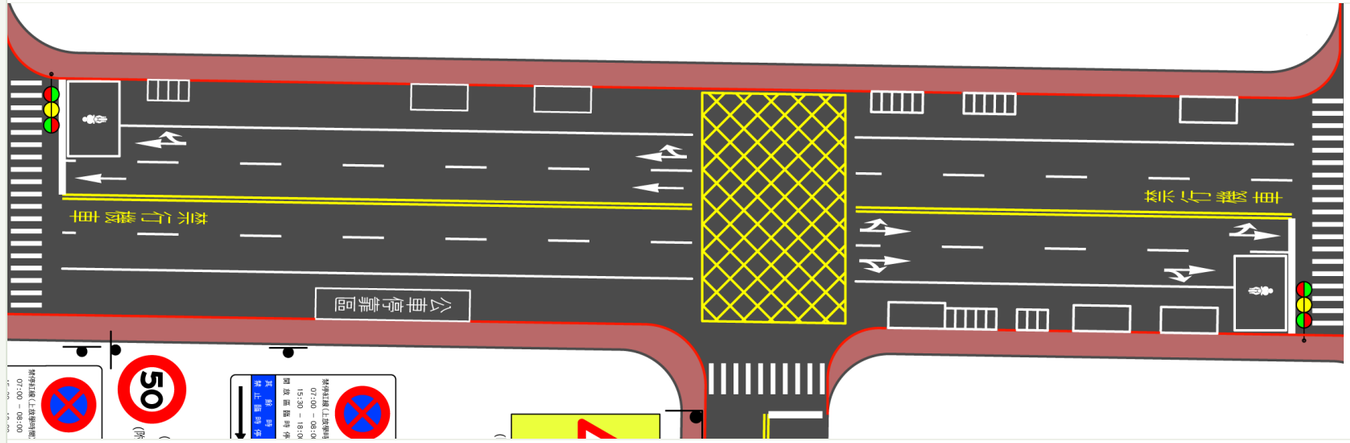

現況圖・路口範圍

主要道路 / 現況	28 m	雙向 6 車道（含慢車道）　路段速限 50 km/h
次要道路 / 現況	14 m	雙向 2 車道　路段速限 30 km/h

本例改善目標

01 **明確化次要道路管制**

缺少明確的停管制提示時，主要與次要道路的關係不易辨識。

02 **提升行人穿越安全**

縮短行人穿越暴露在道路的距離、提升行人穿越明視性。

03 **整理車流與路側空間**

左轉、直行續進、公車與路側停車，應各有清楚位置。


> 若在主要道路設置無號誌行人穿越道，指引建議配合將速限降至 **30 km/h**，或改設為號誌化路口。這是本示例改善配置的前提。

G1-01 / CURRENT CONDITIONS

現況問題

無號誌市區正交三岔路口

現況圖

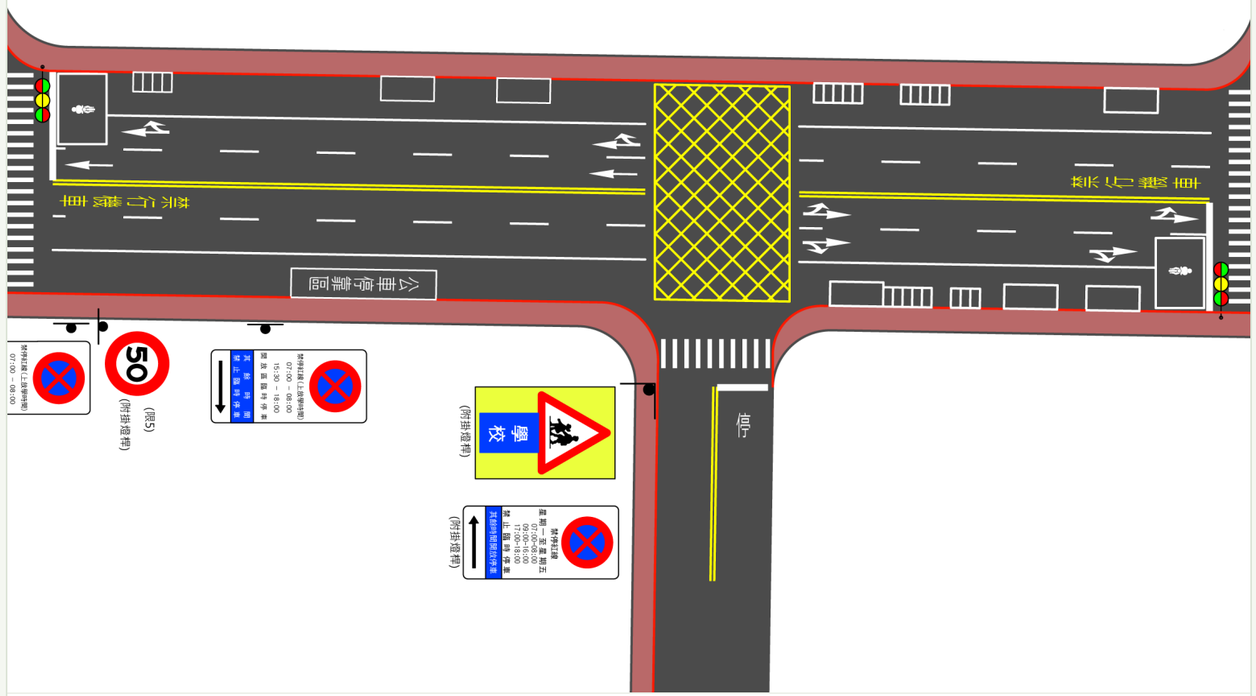

01 停讓提示與行人警示



- 次要道路僅設「停」標字。
- 前方設有行穿線，建議加設「當心行人」標誌。
- 路側空間足夠時，搭配「停車再開」標誌。

02 檢視標誌是否符合環境




- 周邊學校為國中，「當心兒童」的適用情形應重新檢視。
- 次要道路未設「最高速限」標誌。

G1-01 / SCENARIO OVERVIEW

整體佈設策略

G1-01 / 市區・正交

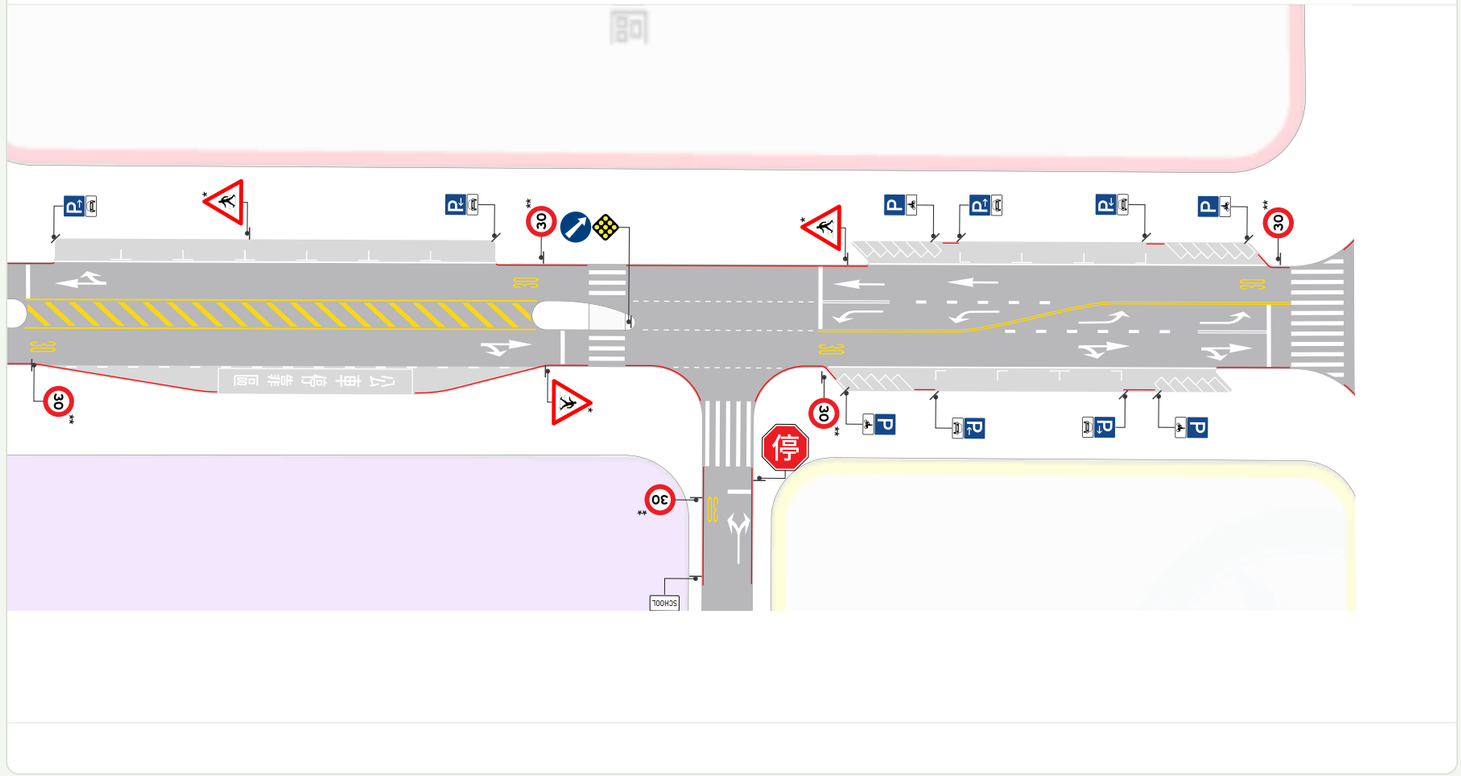

從路面邊線到標誌配置，將同一個路口的設置考量串成完整的解說。

01 界定行車與路側空間 §183 / §190 ↗

02 增加行人穿越警告標誌 §185 / §41 ↗

03 引導直行與轉彎動線 §188 / §189 / §189-1 ↗

04 傳達速限與學校環境 §85 / §126 ↗

M1-01 M1-03 M2-01 M2-04 M3-01 M3-04 M4-01

相關模組：路口動線、路側停車、停讓管制、行向管制、行人、公車及危險警示。


G1-01 / MARKING APPLICATION

標線條文運用解說

G1-01 / 市區・正交

01 / 09　標線

G1-01 / 路面邊線

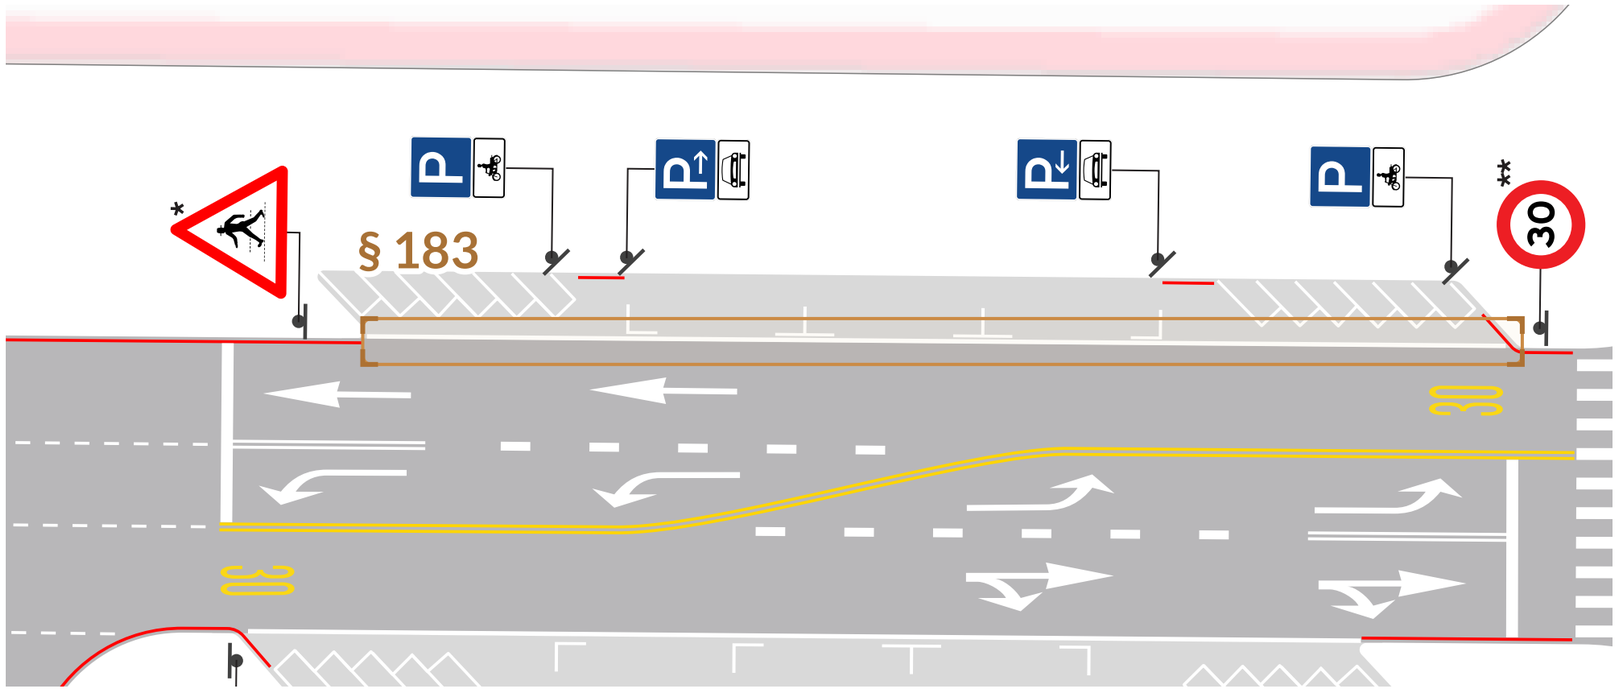

《設置規則》§ 183

路面邊線

01 作為最右側車道的行車導引，界定行車道與路側服務空間。

02 建議車輛停放線與路面邊線保留約 30 cm 緩衝，並讓路段邊線接續路口轉角的邊線。

03 路面邊線為 15 cm；應與 10 cm 的快慢車道分隔線區分。


G1-01 / MARKING APPLICATION

標線條文運用解說

G1-01 / 市區・正交

02 / 09　標線

G1-01 / 枕木紋行人穿越道線

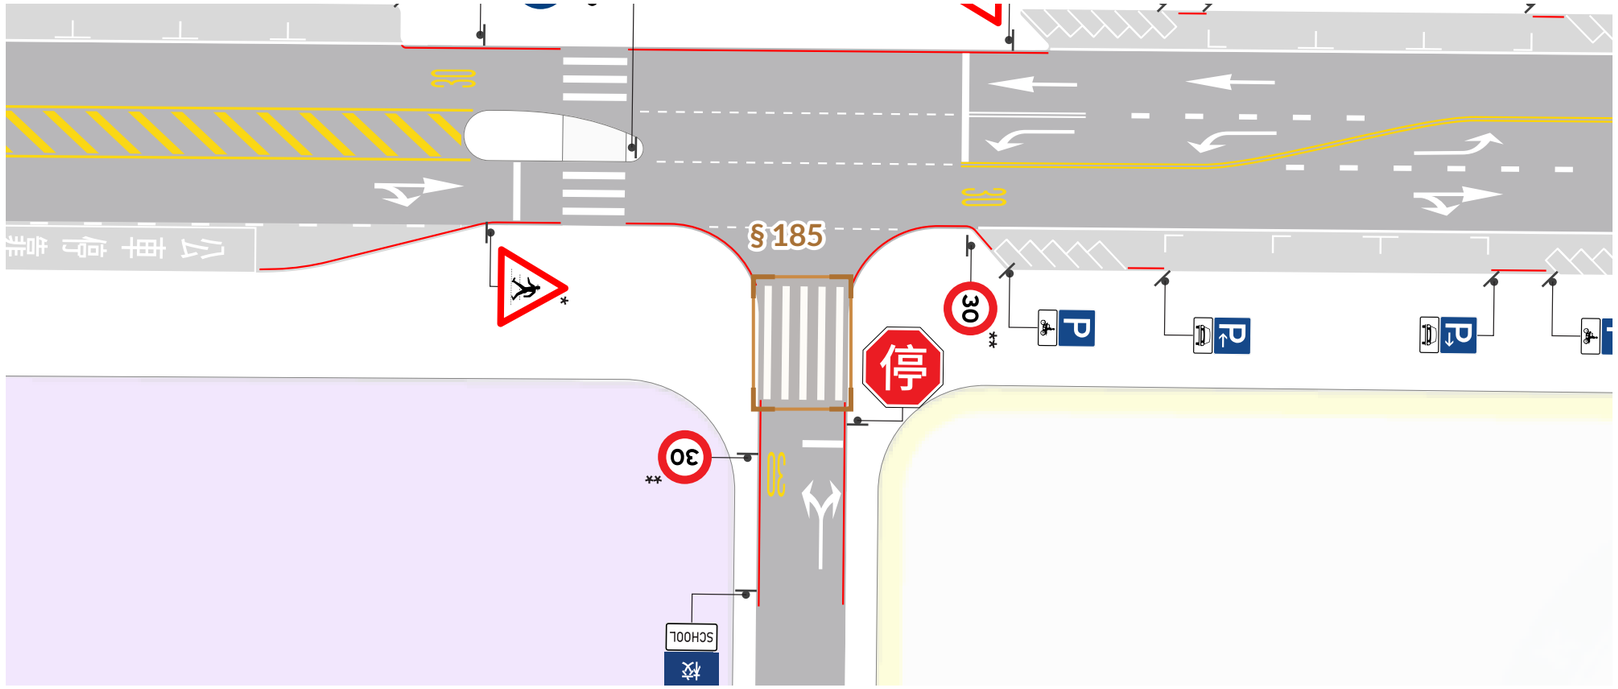

《設置規則》§ 185

枕木紋行人穿越道線

01　可配合設置當心行人標誌「警34」警告車輛注意行人通過。

02　枕木紋平行車流方向劃設。

03　枕木紋行人穿越道線與停止線建議 2 至 3 m。


G1-01 / MARKING APPLICATION

標線條文運用解說

G1-01 / 市區・正交

03 / 09　標線

G1-01 / 指向線

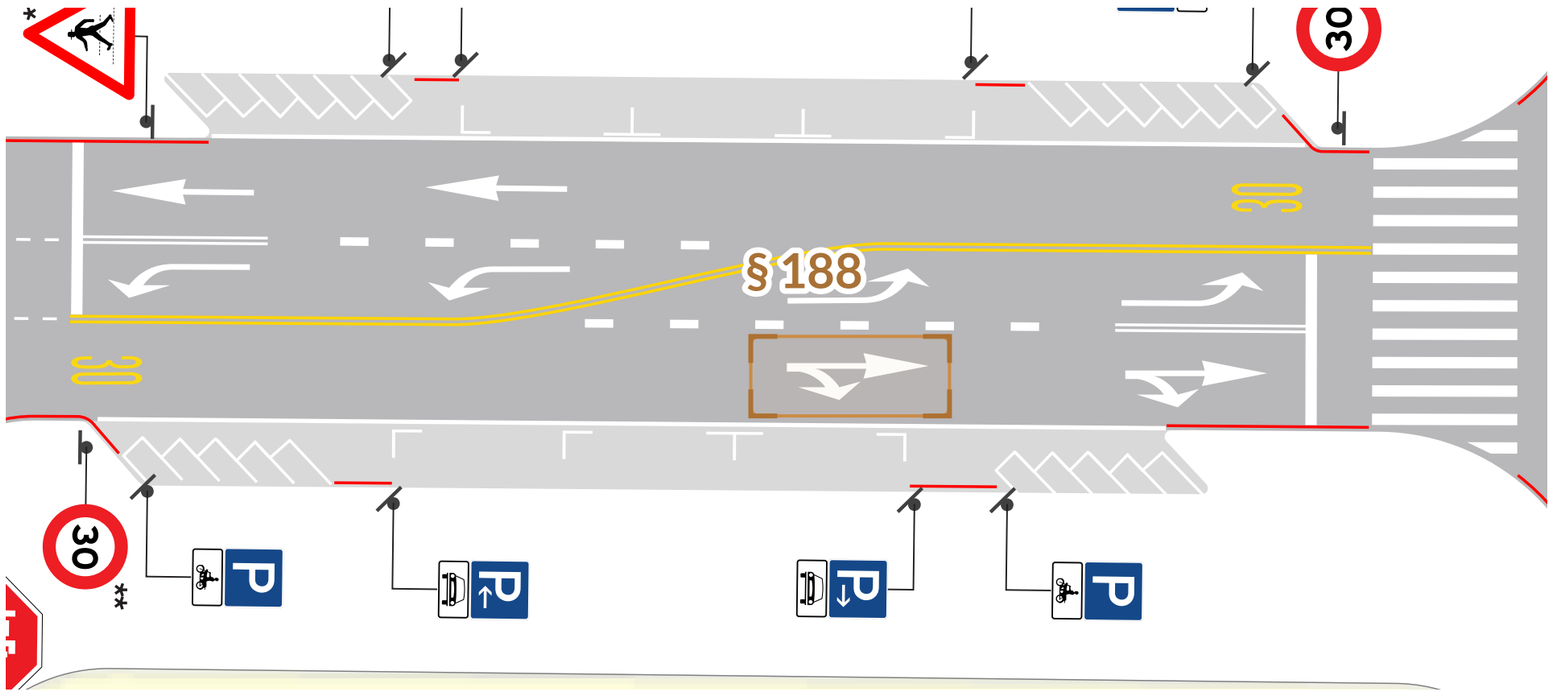

《設置規則》§ 188

指向線

01 本示例直右共用混合車道寬度為 3.5 m 以下，使用直線與弧形合併的分岔箭頭。

02 車道寬度為 3.5 m 以上時，使用直線與弧形分離、並列的分流式指向線。


G1-01 / MARKING APPLICATION

標線條文運用解說

G1-01 / 市區・正交

04 / 09　標線

G1-01 / 路口行車導引線

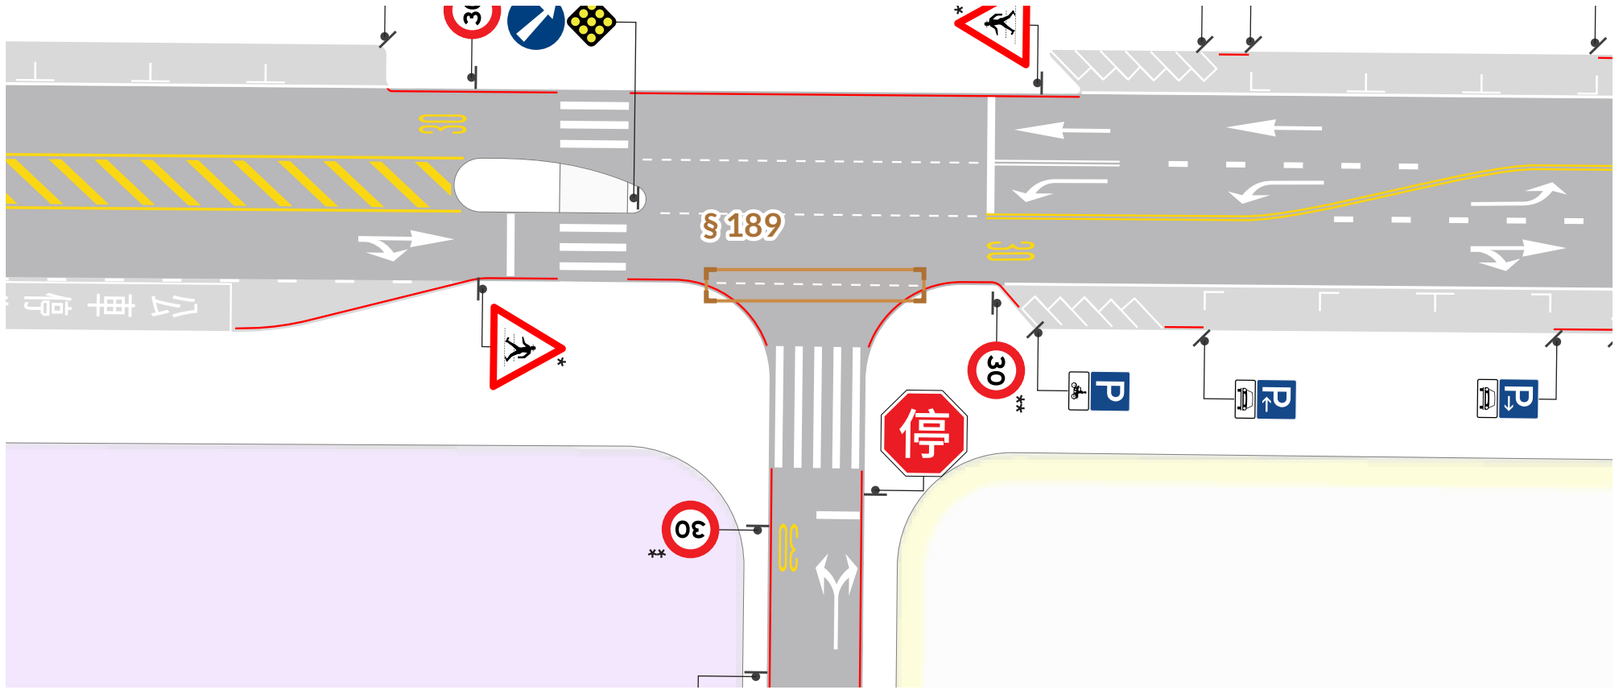

《設置規則》§ 189

路口行車導引線

01 於主要道路通過次要道路的路口右側繪設，彰顯主要道路車流方向。

02 路口行車導引線應與主要道路兩端的路面邊線相連接，讓直行動線清楚延續。

03 右側導引線也提供次要道路車輛進入路口前觀察主要道路車流的位置。


G1-01 / MARKING APPLICATION

標線條文運用解說

G1-01 / 市區・正交

05 / 09　標線

G1-01 / 穿越虛線

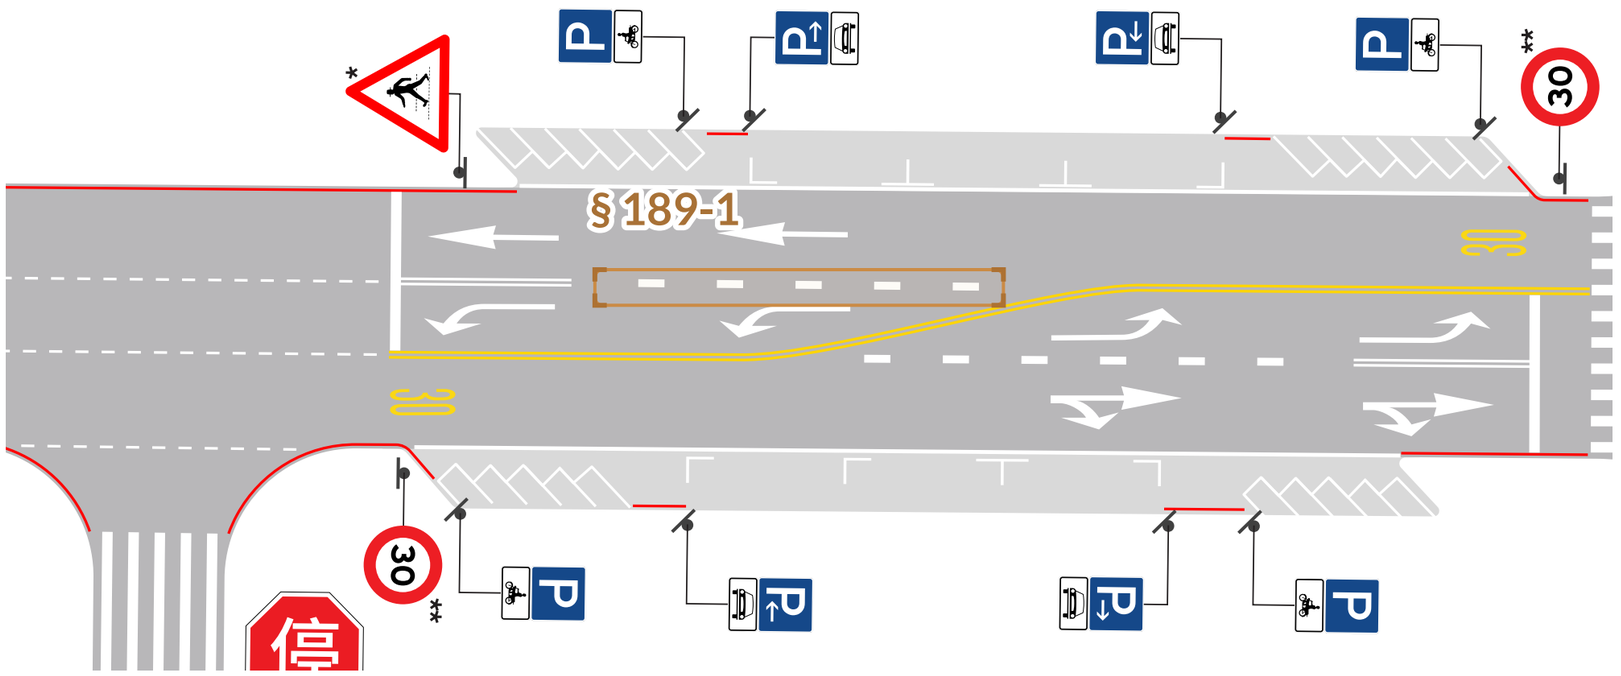

《設置規則》§ 189-1

穿越虛線

01 由 1直行車道轉換為直行、左轉 2 車道時，提示左轉車可匯出至專用道。


02 原則上由漸變區起點劃至專用車道起點，提示左轉車打方向燈並分流。

03 本例屬市區道路，漸變長度依《市區道路及附屬工程設計規範》第 4.2.6 節；省道公路另依《公路路線設計規範》第 4.2.10 節。

G1-01 / MARKING APPLICATION

標線條文運用解說

G1-01 / 車輛停放線

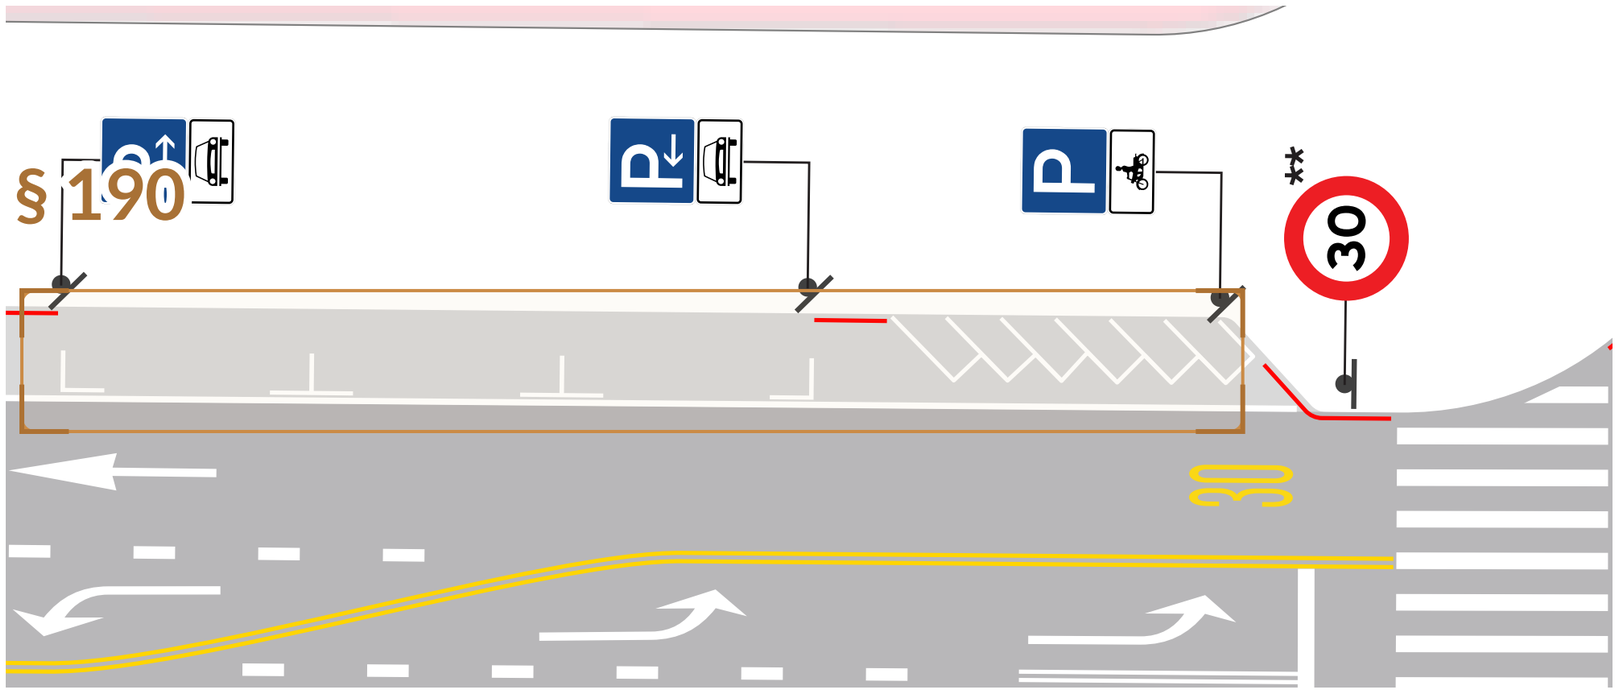

《設置規則》§ 190

車輛停放線


01 建議靠近路口先配置大型重型機車以外的機車停放線，再配置其他車種格位。

02 建議佈設於距橫交道路緣延伸處 10 至 30 m 以外，保留路口空間。

G1-01 / SIGNAGE APPLICATION

標誌條文

G1-01 / 當心行人標誌

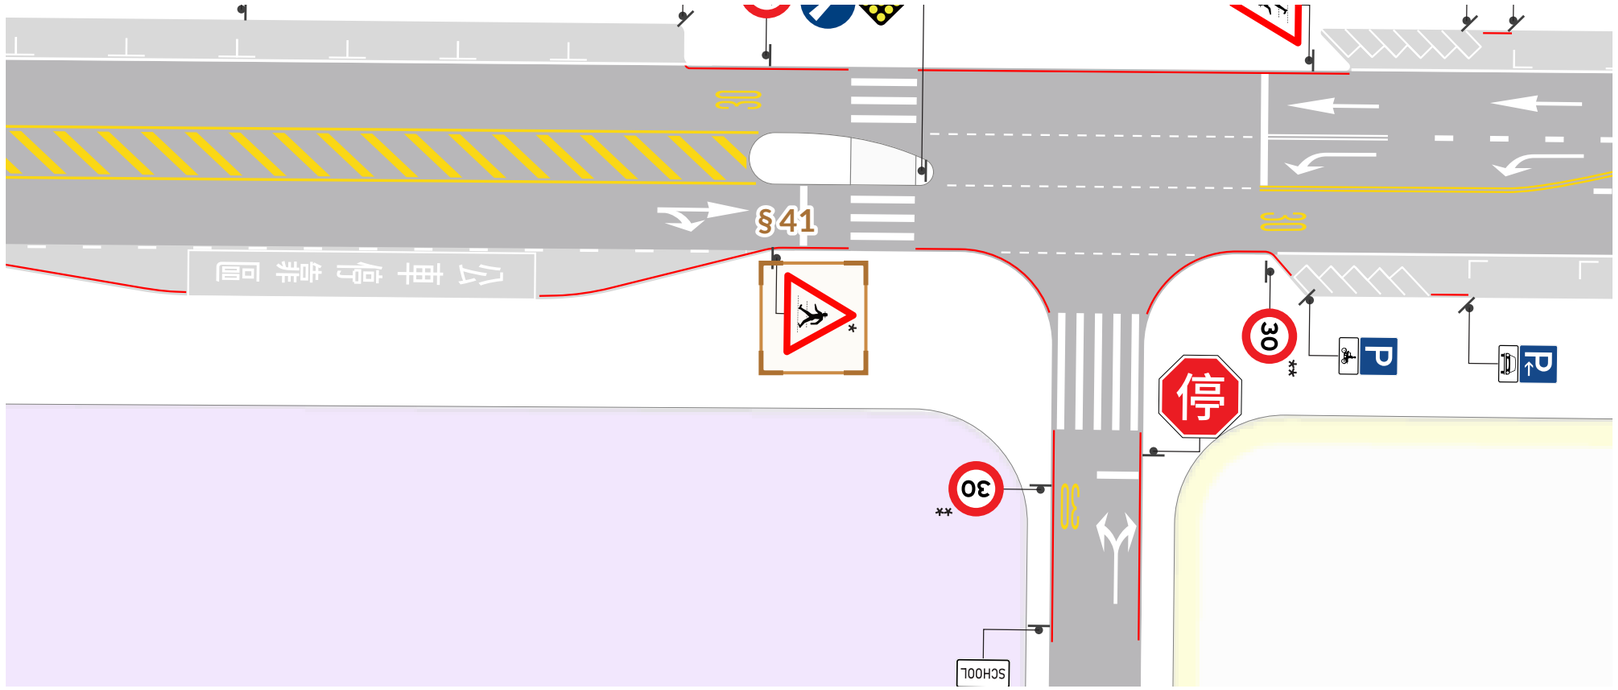

《設置規則》§ 41

當心行人標誌

01　建議警34設於距行穿線上游停車視距處。


02　可與其他標誌共桿，並加設「減速慢行暫停讓行人」附牌。

03　亦可於上游距行穿線約 30 m 再增設一面，附「前方30 m」，並依行車速限與最短安全視距增加。

G1-01 / SIGNAGE APPLICATION

標誌條文

G1-01 / 最高速限標誌

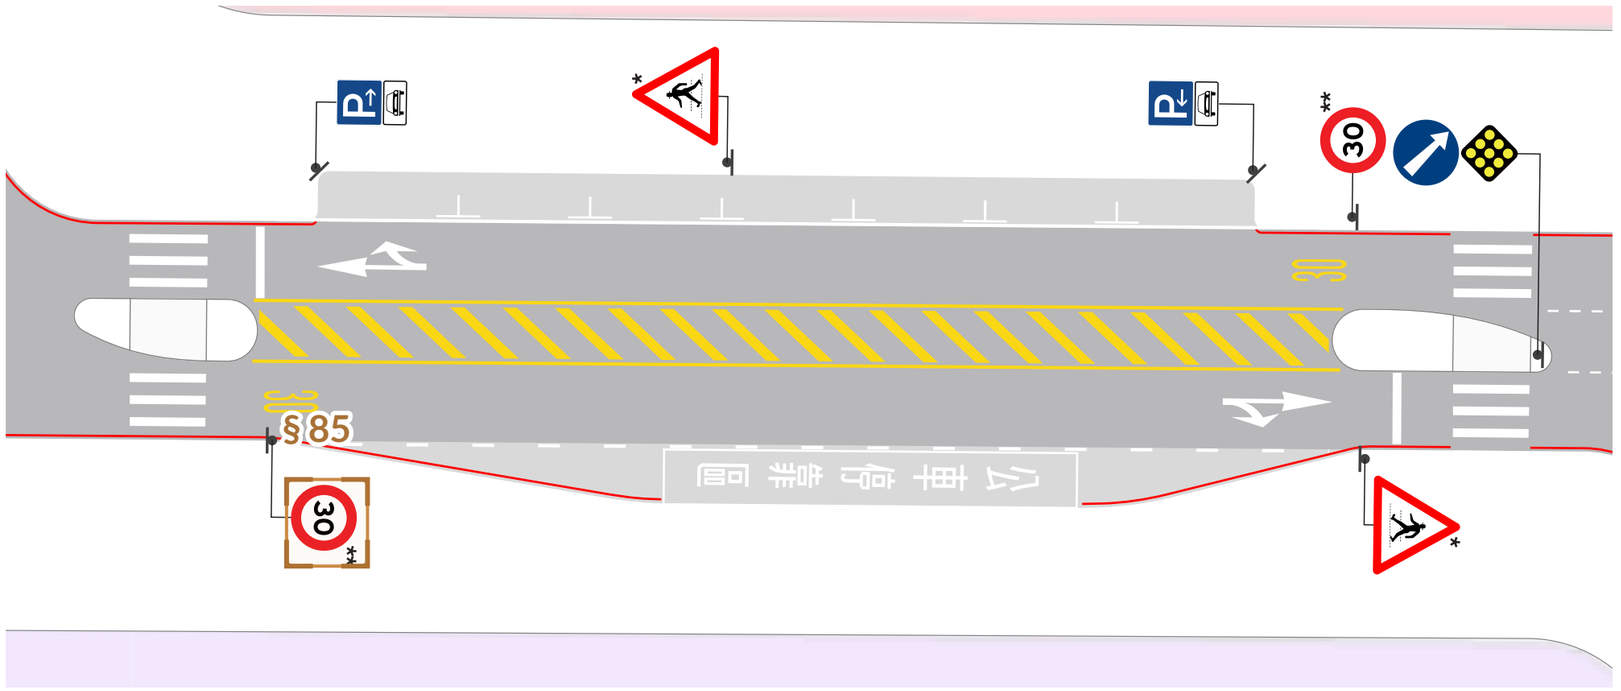

G1-01 / 市區・正交

08 / 09 標誌

《設置規則》§ 85

最高速限標誌


01 本示例建議設於路口（即下游）遠端，速限變更處應能清楚辨識。

02 若上、下游速限相同，則可不重複設置。若重複提示時，得與遠端號誌共桿。

G1-01 / SIGNAGE APPLICATION

標誌條文

G1-01 / 學校標誌

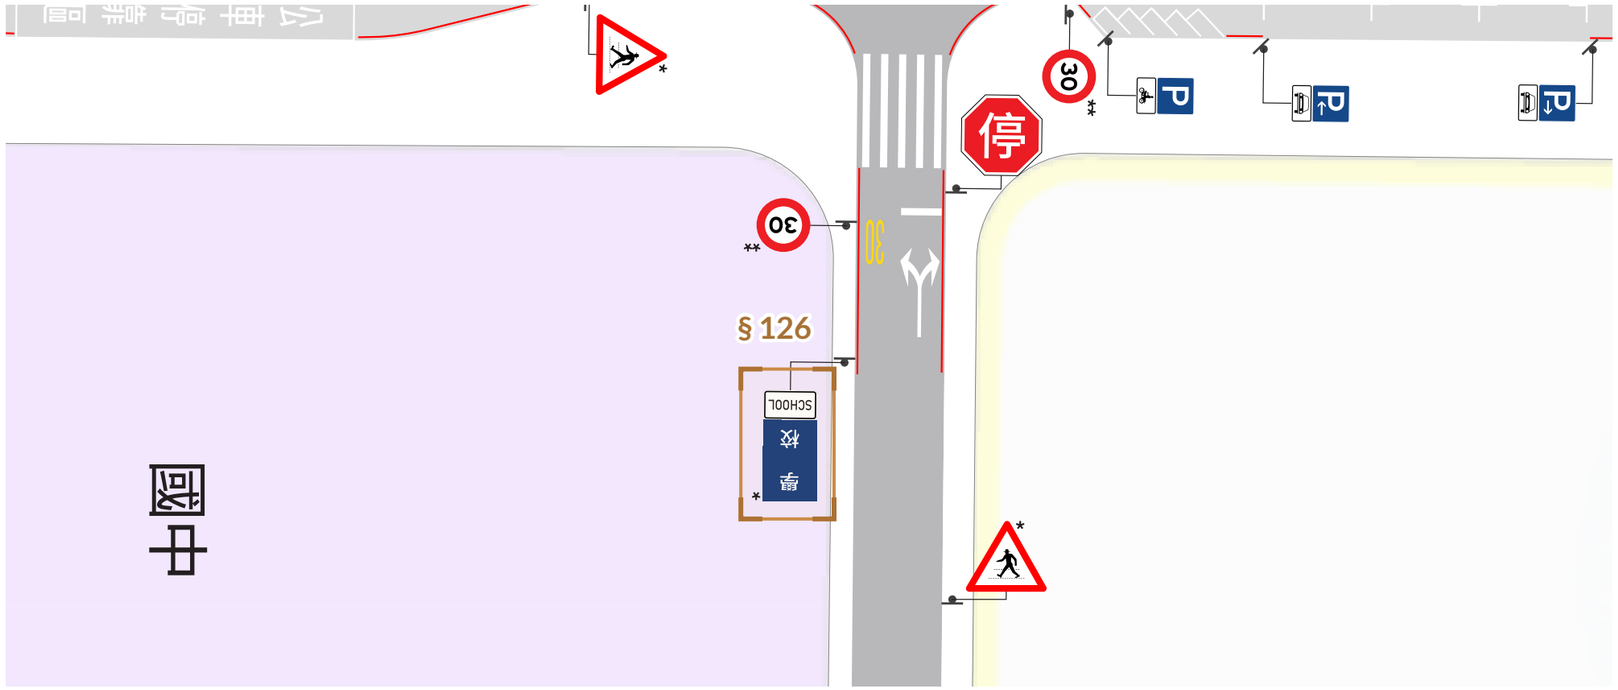

《設置規則》§ 126

學校標誌

01 路口周邊有學校時，指引建議設置學校標誌，提醒駕駛嘺聲慢行。

02 標誌宜垂直行車方向，設於駕駛不易辨識前方為學校附近之處。

03 考量外國人士識別，可加設英文附牌，提高告示效果。