
M1-01.1 · 2 / 3

路口與路段車道配置｜圖例說明

以標線與預告標誌，逐步說清楚各方向的車道與行進路徑。

路口與路段車道配置

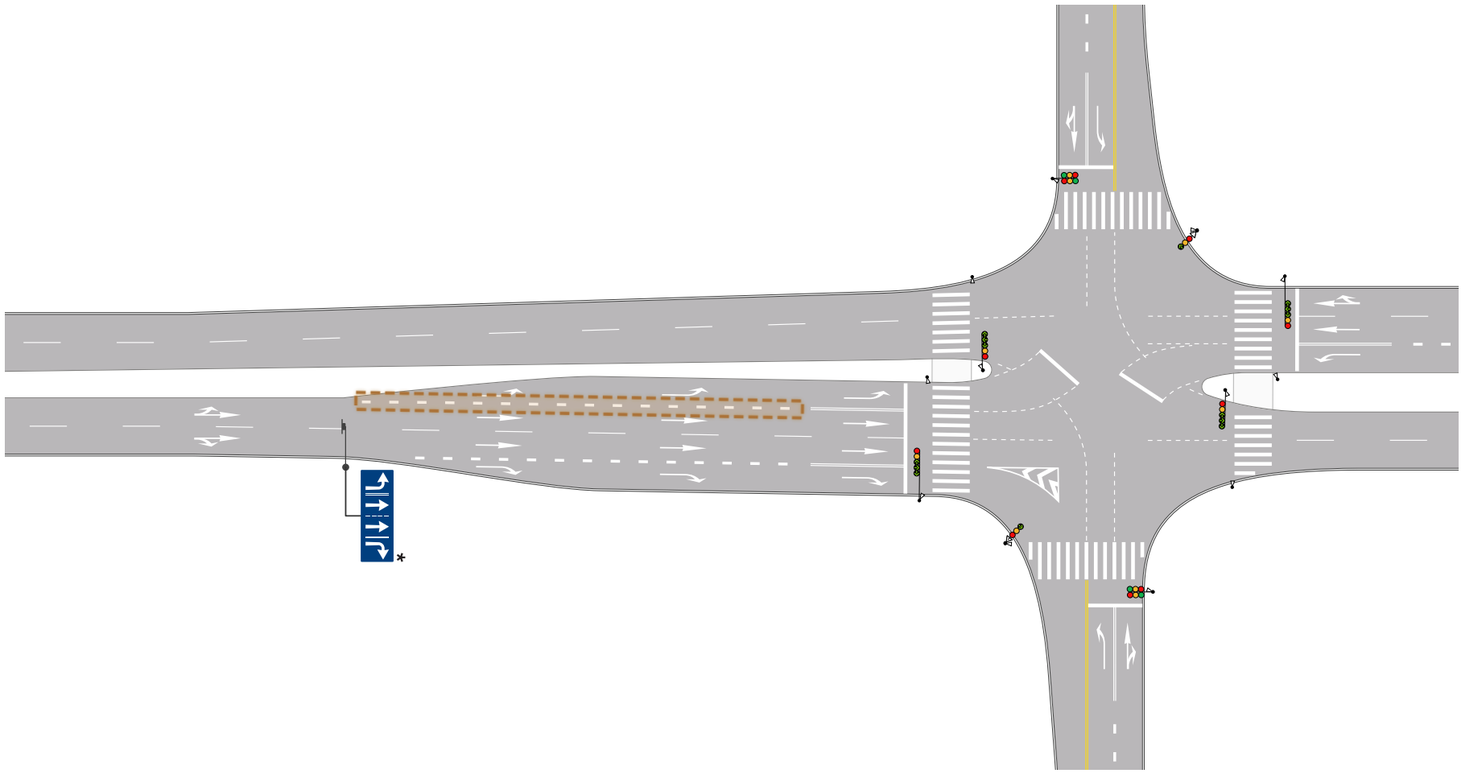

穿越虛線

01 **穿越虛線區分直行與轉向**

匯入主線建議採 15 cm 寬；匯出主線建議採 30 cm 寬，加強交織提示。

02 **從漸變區引導至專用車道**

穿越虛線由漸變區起點延伸至專用車道起點；左右轉專用道進入路口前 20 m 搭配禁止變換車道線。