
M1-01.1 · 2 / 3

路口與路段車道配置｜圖例說明

以標線與預告標誌，逐步說清楚各方向的車道與行進路徑。

路口與路段車道配置

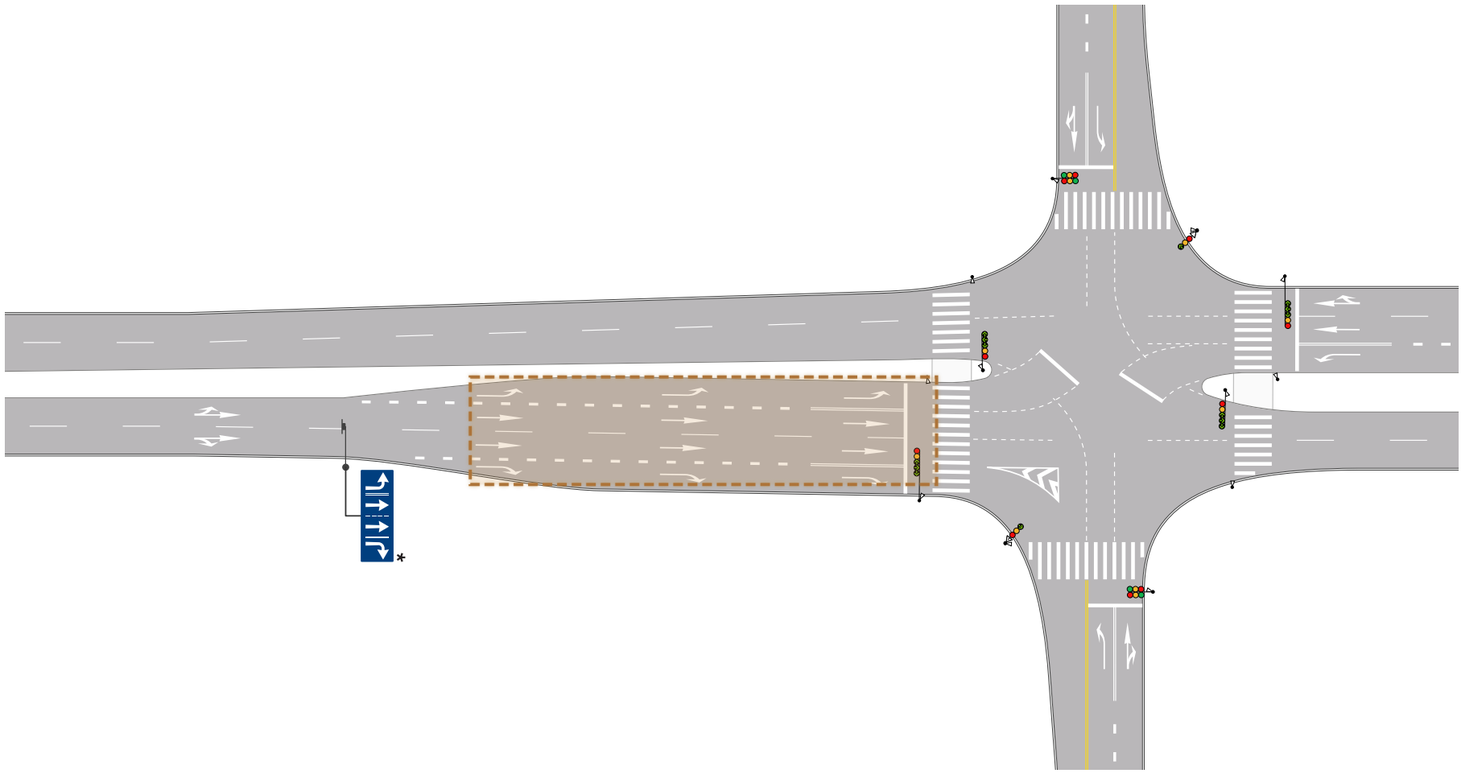

指向線

01 **指向線分組預告**

第一組設於停止線或機慢車停等區外邊界上游 2–5 m；第二組再往上游 20 m，其後各組間隔 20–60 m。