
M1-01.2 · 2 / 3

附加車道｜圖例說明

從漸變區開始，連續提示轉向車道的位置與用途。

附加車道配置

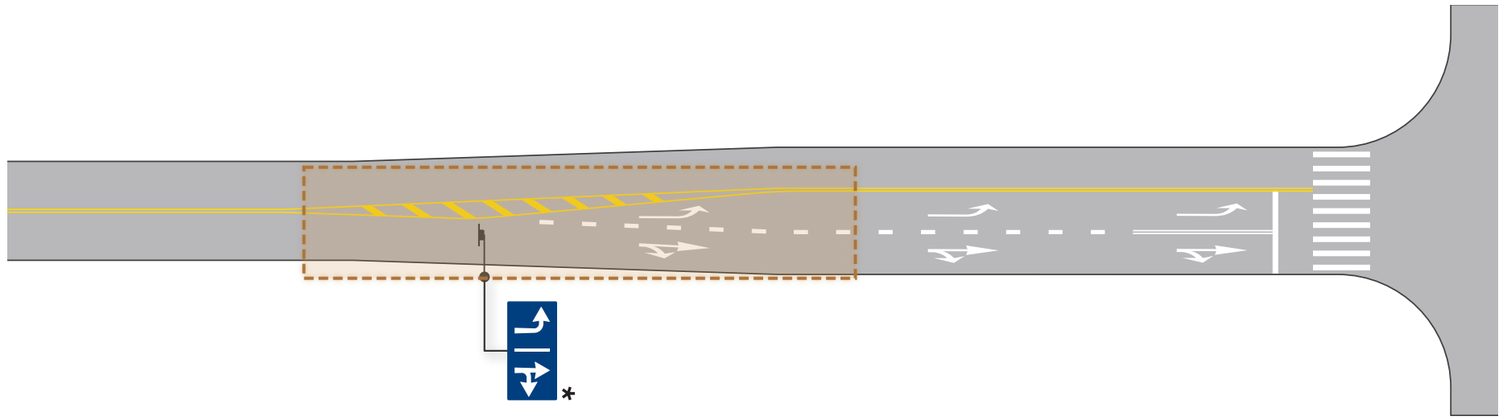

漸變長度

01 依設計速率安排漸變長度

市區道路依設計規範第 4.2.6 節檢核，設計速率與漸變段長寬比對照如下。

設計速率（km/h）	漸變段長寬比
20	3:1
30	4:1
40	6:1
50	8:1
60	10:1
70	12:1
80	14:1
90	15:1