
M1-01.2 · 2 / 3

附加車道｜圖例說明

從漸變區開始，連續提示轉向車道的位置與用途。

錯位 T 字路口漸變段指向線

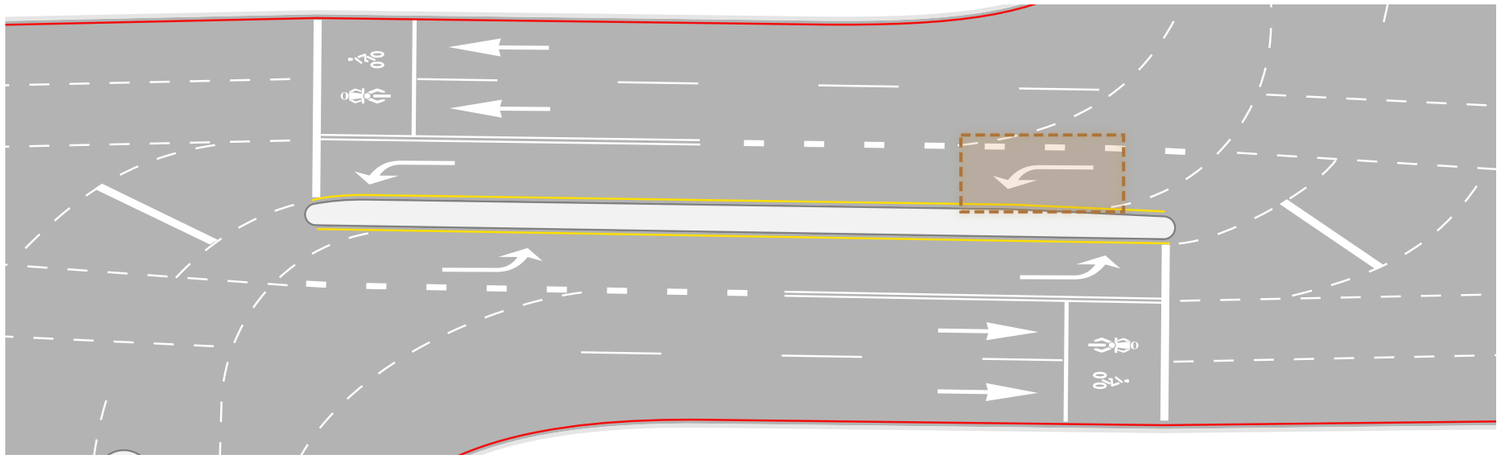

指向線

01 **漸變起點就提示轉向**

左轉或右轉附加車道在漸變起點劃設相應指向線；空間足夠時，各車道的指向線位置宜統一。

02 **錯位 T 字路口配合實際動線**

左轉車道開始附加時劃設左轉指向線；同一斷面的直行車道若上下游順接、無選道疑慮，可不另設直行指向線。